
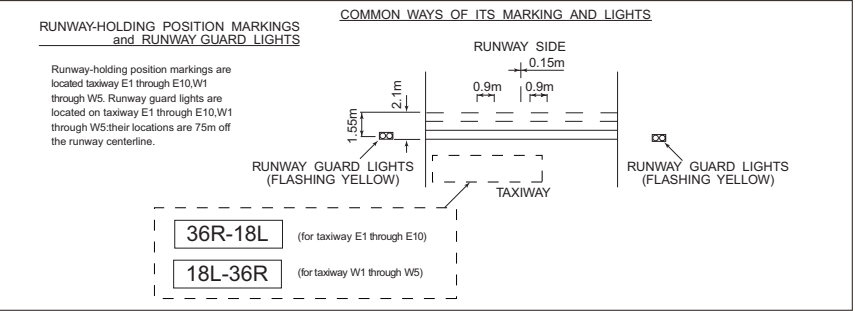


AERODROME CHART

NAHA AIRPORT  
ELEV 11ft (3.3m)

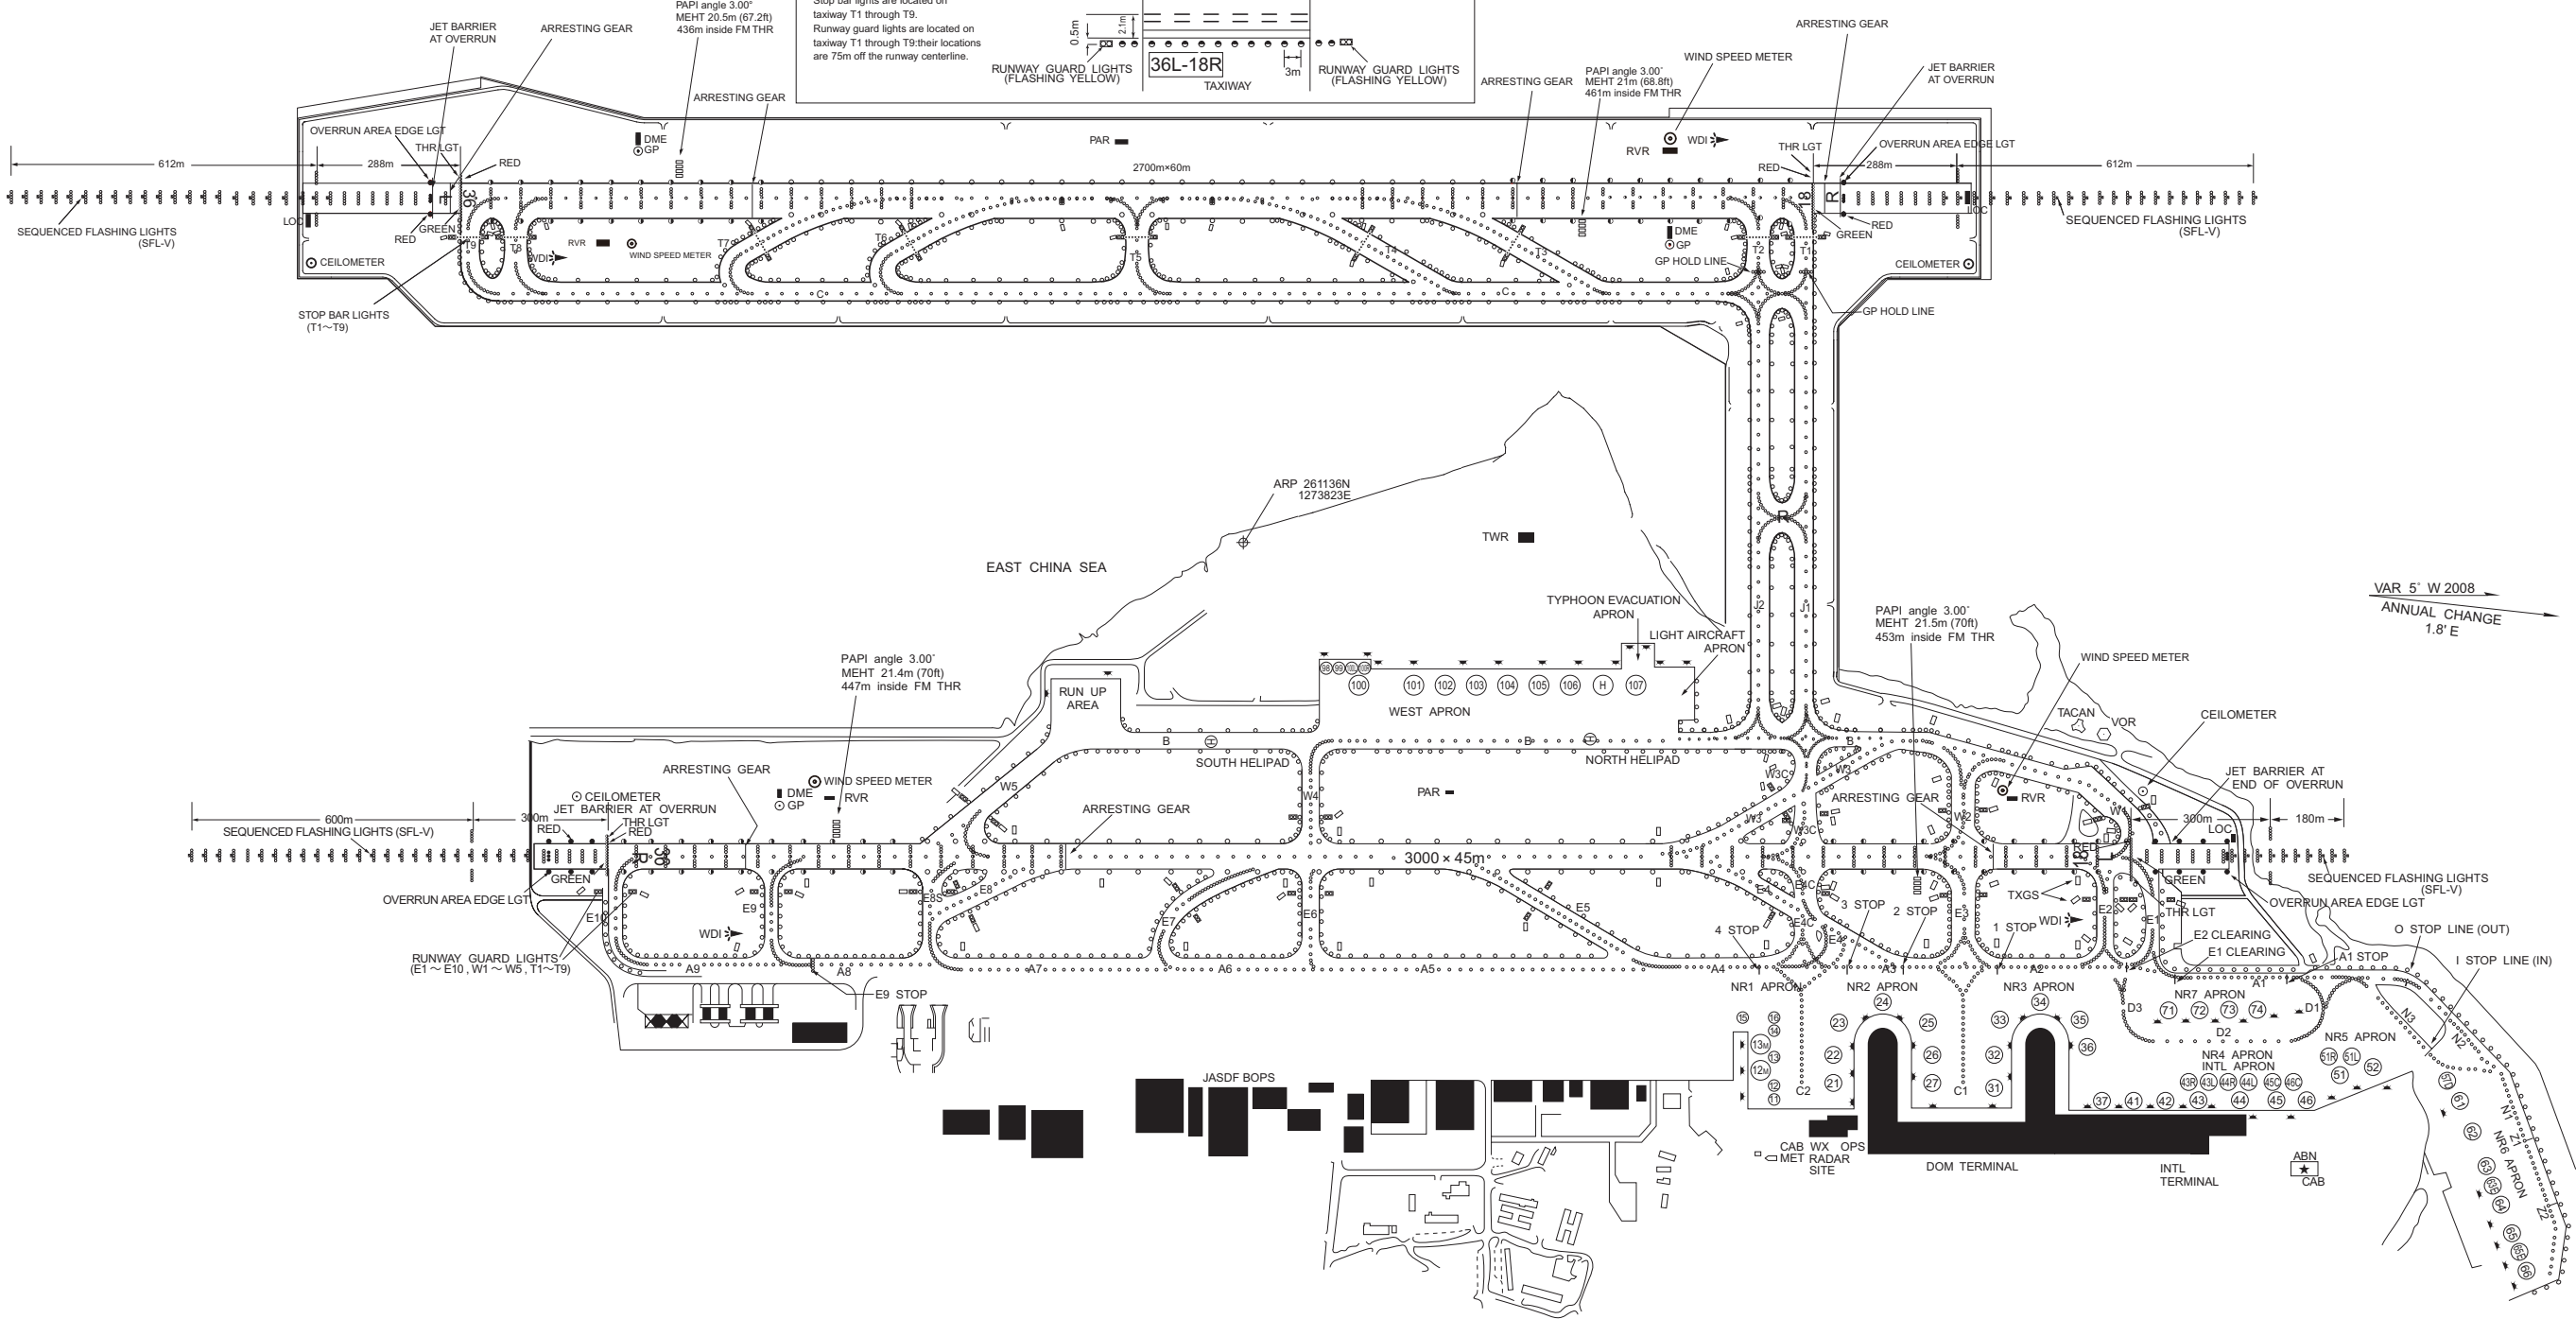

CHANGE : TWY D3 installed.